COMUNE DI NAPOLI

ELABORATI GRAFICI

per S.C.I.A. Sanitaria

COMMITTENTE : A.P.L. S.r.l.

INDIRIZZO: via Saverio Altamura nn. 21-23

ATTIVITA': Ristorante e Pizzeria

SCALA : 1:100


DATA : 3 Marzo 2020

Il tecnico
Geom. Angelo Bongo



GRAFICI QUOTATI

scala 1:100

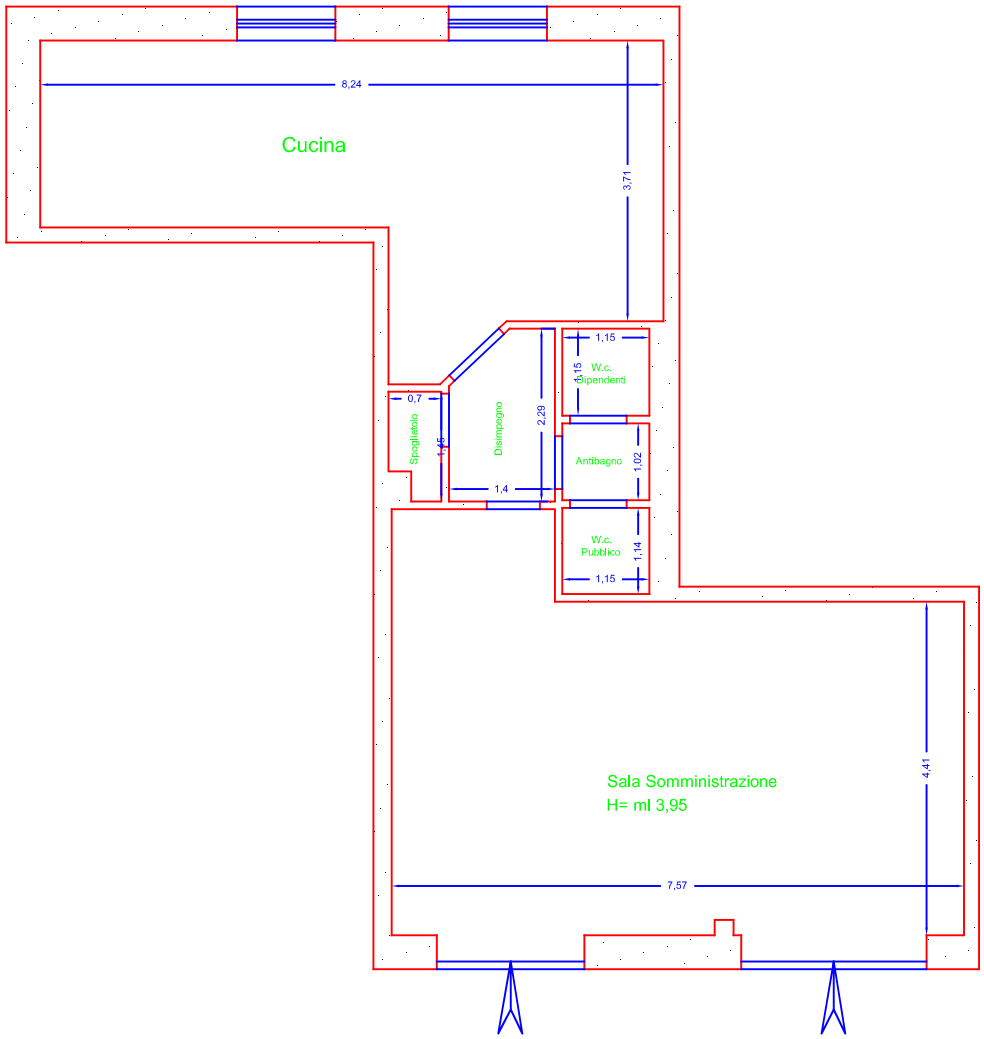


Via Saverio Altamura nn. 21-23

LEGENDA SUPERFICI		
SALA SOMMINISTRAZIONE	mq	37,96
DISIMPEGNO	mq	2,89
SPOGLIATOIO	mq	0,96
ANTIBAGNO	mq	1,24
W.C. DIPENDENTI	mq	1,39
W.C. PER IL PUBBLICO	mq	1,39
CUCINA	mq	25,80
SUPERFICIE TOTALE	mq	71,63



LAYOUT ARREDO E ATTREZZATURE

scala 1:100

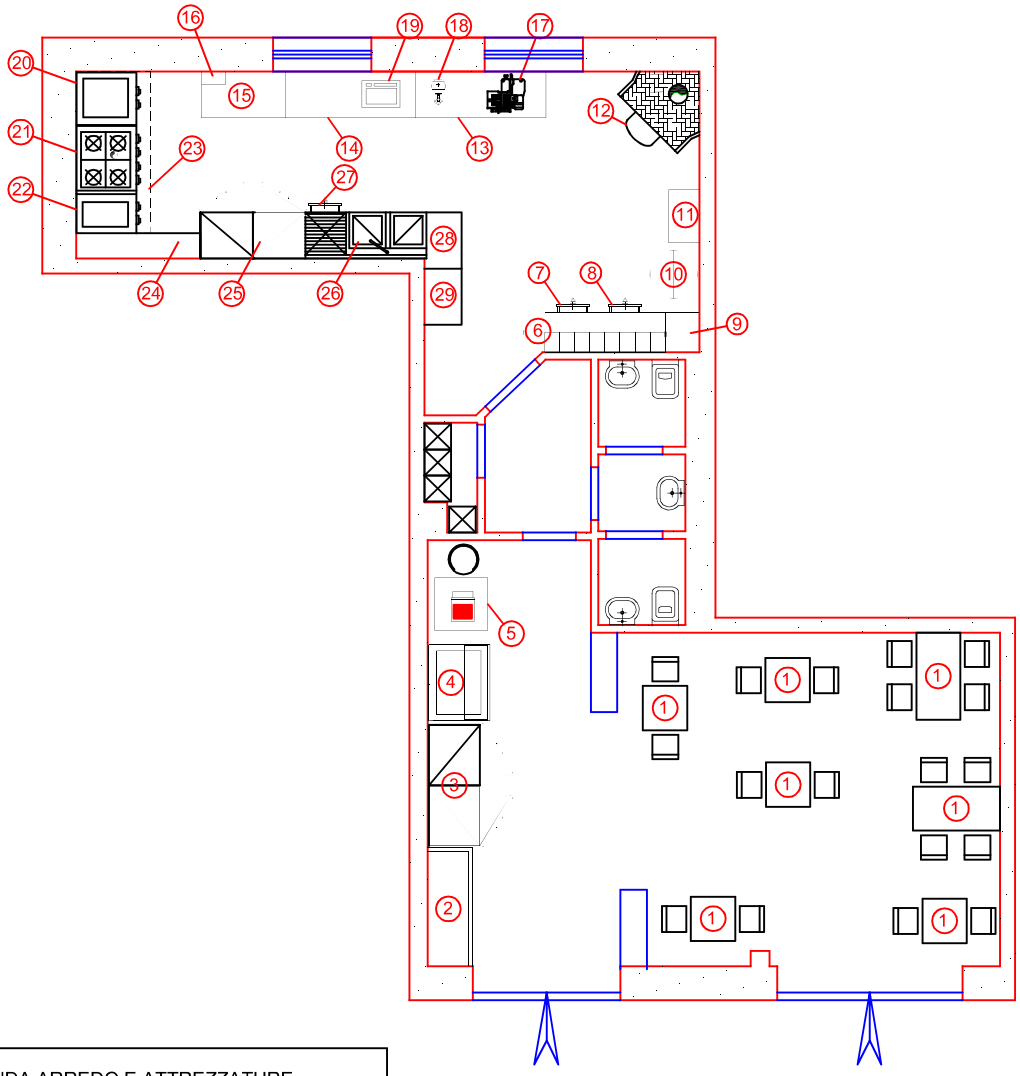

LEGENDA ARREDO E ATTREZZATURE			
ITEM	DESCRIZIONE	ITEM	DESCRIZIONE
1	TAVOLI CON SEDIE	16	LAVELLO
2	CREDENZA POSATE E BIANCHERIA	17	AFFETTATRICE
3	FRIGO BIBITE DOPPIA ANTA	18	GRATTUGIA
4	VETRINA CONTORNI	19	BILANCIA
5	CASSA CON SEDIA ERGONOMICA	20	PIASTRA
6	BANCO PIZZA	21	CUCINA 4 FUOCHI
7	DEPOSITO LEGNO	22	FRIGGITRCE
8	DEPOSITO FARINA	23	CAPPA ECOLOGICA
9	DISPENSA ALIMENTARE	24	BANCO APPOGGIO STOVIGLIE
10	IMPASTATRICE	25	ARMADIO FRIGO 2 ANTE
11	BANCO D'APPOGGIO	26	DOPPIO LAVELLO CON GOCCIOLATOIO PER ALIMENTI
12	FORNO A LEGNA	27	LAVASTOVIGLIE
13	BANCO PIZZERIA	28	BANCO IN ACCIAIO
14	BANCO PER CUCINA	29	MACCHINA PER IL GHIACCIO
15	RUSCIO' PIATTI E POSATE		

Via Saverio Altamura nn. 21-23

