COMUNE DI NAPOLI

Direzione Centrale Sviluppo Economico, Ricerca e mercato del lavoro
Servizio Polizia Amministrativa
Piazza Cavour 42 - 80137 NAPOLI

RILASCIO DELLA CONCESSIONE DI SUOLO PUBBLICO ANNESSO A PUBBLICI ESERCIZI

- DOMANDA DI OCCUPAZIONE CONTINUATIVA -

art.3, c.1, lett.c) Regolamento dehors approvato con d. c. n. 71 del 10/12/2014

UBICAZIONE:

Via Santa Chiara n. 25/bis
Unità immobiliare: piano terra
NCEU: Sez. Urb. POR, foglio 1, p.lla 90, sub. 38 cat. C/1

IL RICHIEDENTE:

Arab foodstuff co. di Omar Suleiman s.a.s
Piazza Vincenzo Bellini, 64 - 80100 Napoli NA
P.IVA 07016310638
Legale rapp: OMAR SULEIMAN - CF: SLM MRO 57C18 Z220X

ELABORATO:

ELABORATO GRAFICO

IL TECNICO:


Ing. Flavio Leboffe
STUDIO TECNICO LEBOFFE
Via A. Depretis 88 - 80133 Napoli (NA)
081 060 9262 - 324 9009 835
flavio.leboffe@gmail.com - flavio.leboffe@ingpec.eu

ORDINE INGEGNERI DELLA PROVINCIA DI NAPOLI – Settore Magistrale e Magistrale – FLAVIO LEBOFFE – INGEGNERE CIVILE E AMBIENTALE – SEZIONE A – N° ISCRIZIONE 20759

Napoli, lì 13/11/2025

INQUADRAMENTO TERRITORIALE ED URBANISTICO


INQUADRAMENTO SU STRALCIO AEROFOTOGRAMMETRICO scala 1:2.000

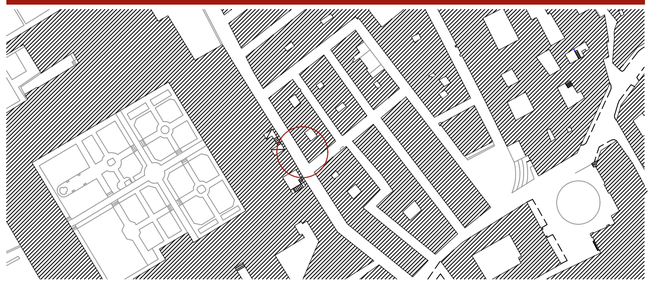


INQUADRAMENTO SU ORTOFOTO



INQUADRAMENTO SU PIANO URBANISTICO COMUNALE

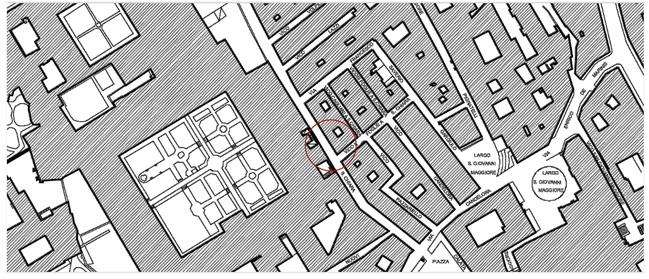


INQUADRAMENTO SU STRALCIO TAVOLA 14 - AREE DI INTERESSE ARCHEOLOGICO

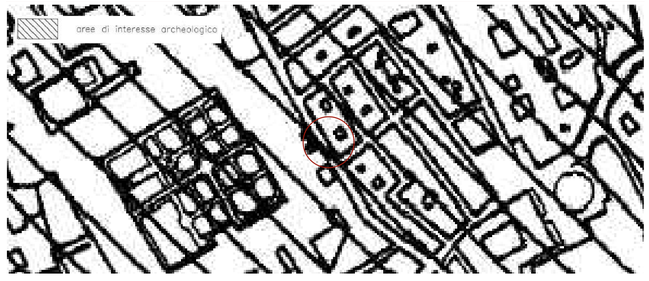

GRAFICI STATO DI FATTO

PLANIMETRIA Via Santa Chiara n°25/bis e area esterna scala 1:100

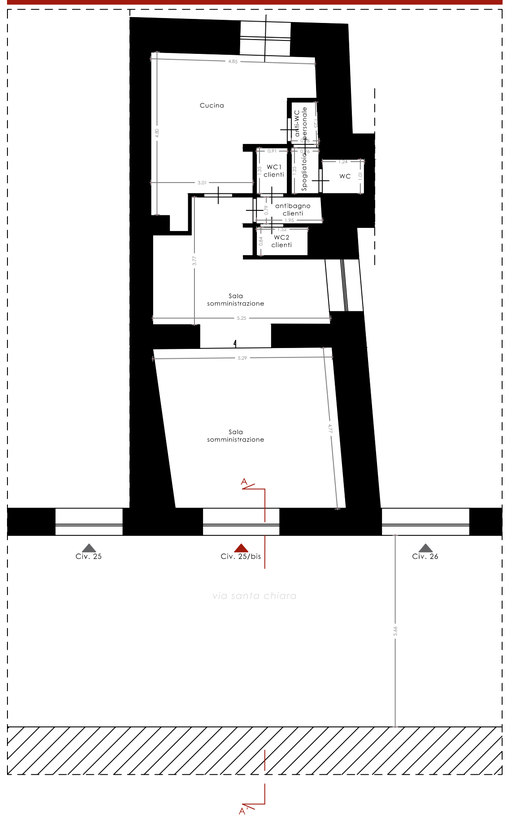

PROSPETTO Via Santa Chiara n°25 bis con area esterna scala 1:100




SEZIONE A-A' scala 1:100




GRAFICI STATO DI PROGETTO

PLANIMETRIA Via Santa Chiara n°25/bis e area esterna scala 1:100

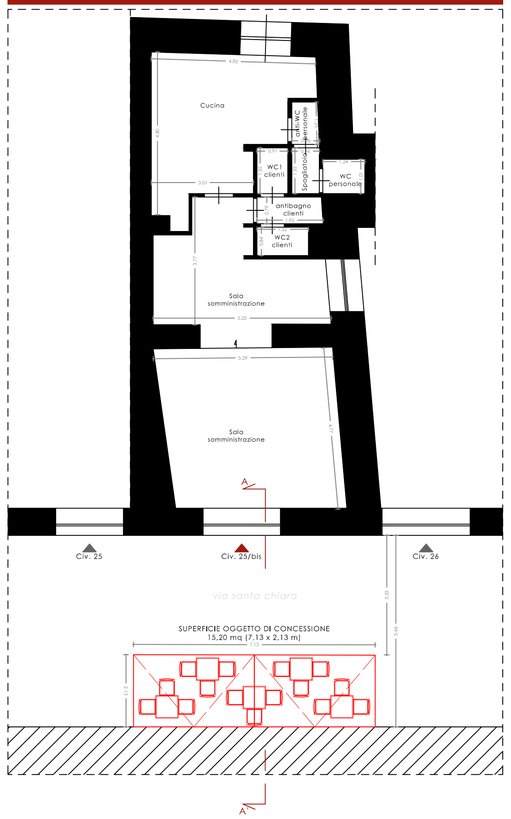

PROSPETTO Via Santa Chiara n°25 bis con area esterna scala 1:100

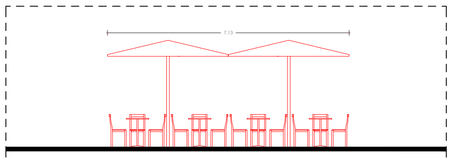

SEZIONE A-A' scala 1:100

