




CONTE
DI
RIVO
49.1
49.3
A
48.1
2961
47.7
47.1
220
PIAZZA BELLINI
COSTANTINOPOLI
40.6
BELLINI
46.3
45.5
4600
VICO COSTANTINOPOLI
MAIELLA
A
S. PIETRO
45.1
43.6
3049
VIA
44.6
VIA
2501
PORT'ALBA
C
46.3
40.2
VIA
3072
VICOLETTO
S. PIETRO
VICOLETTO
3059
36.7
ISTITUTO CASA

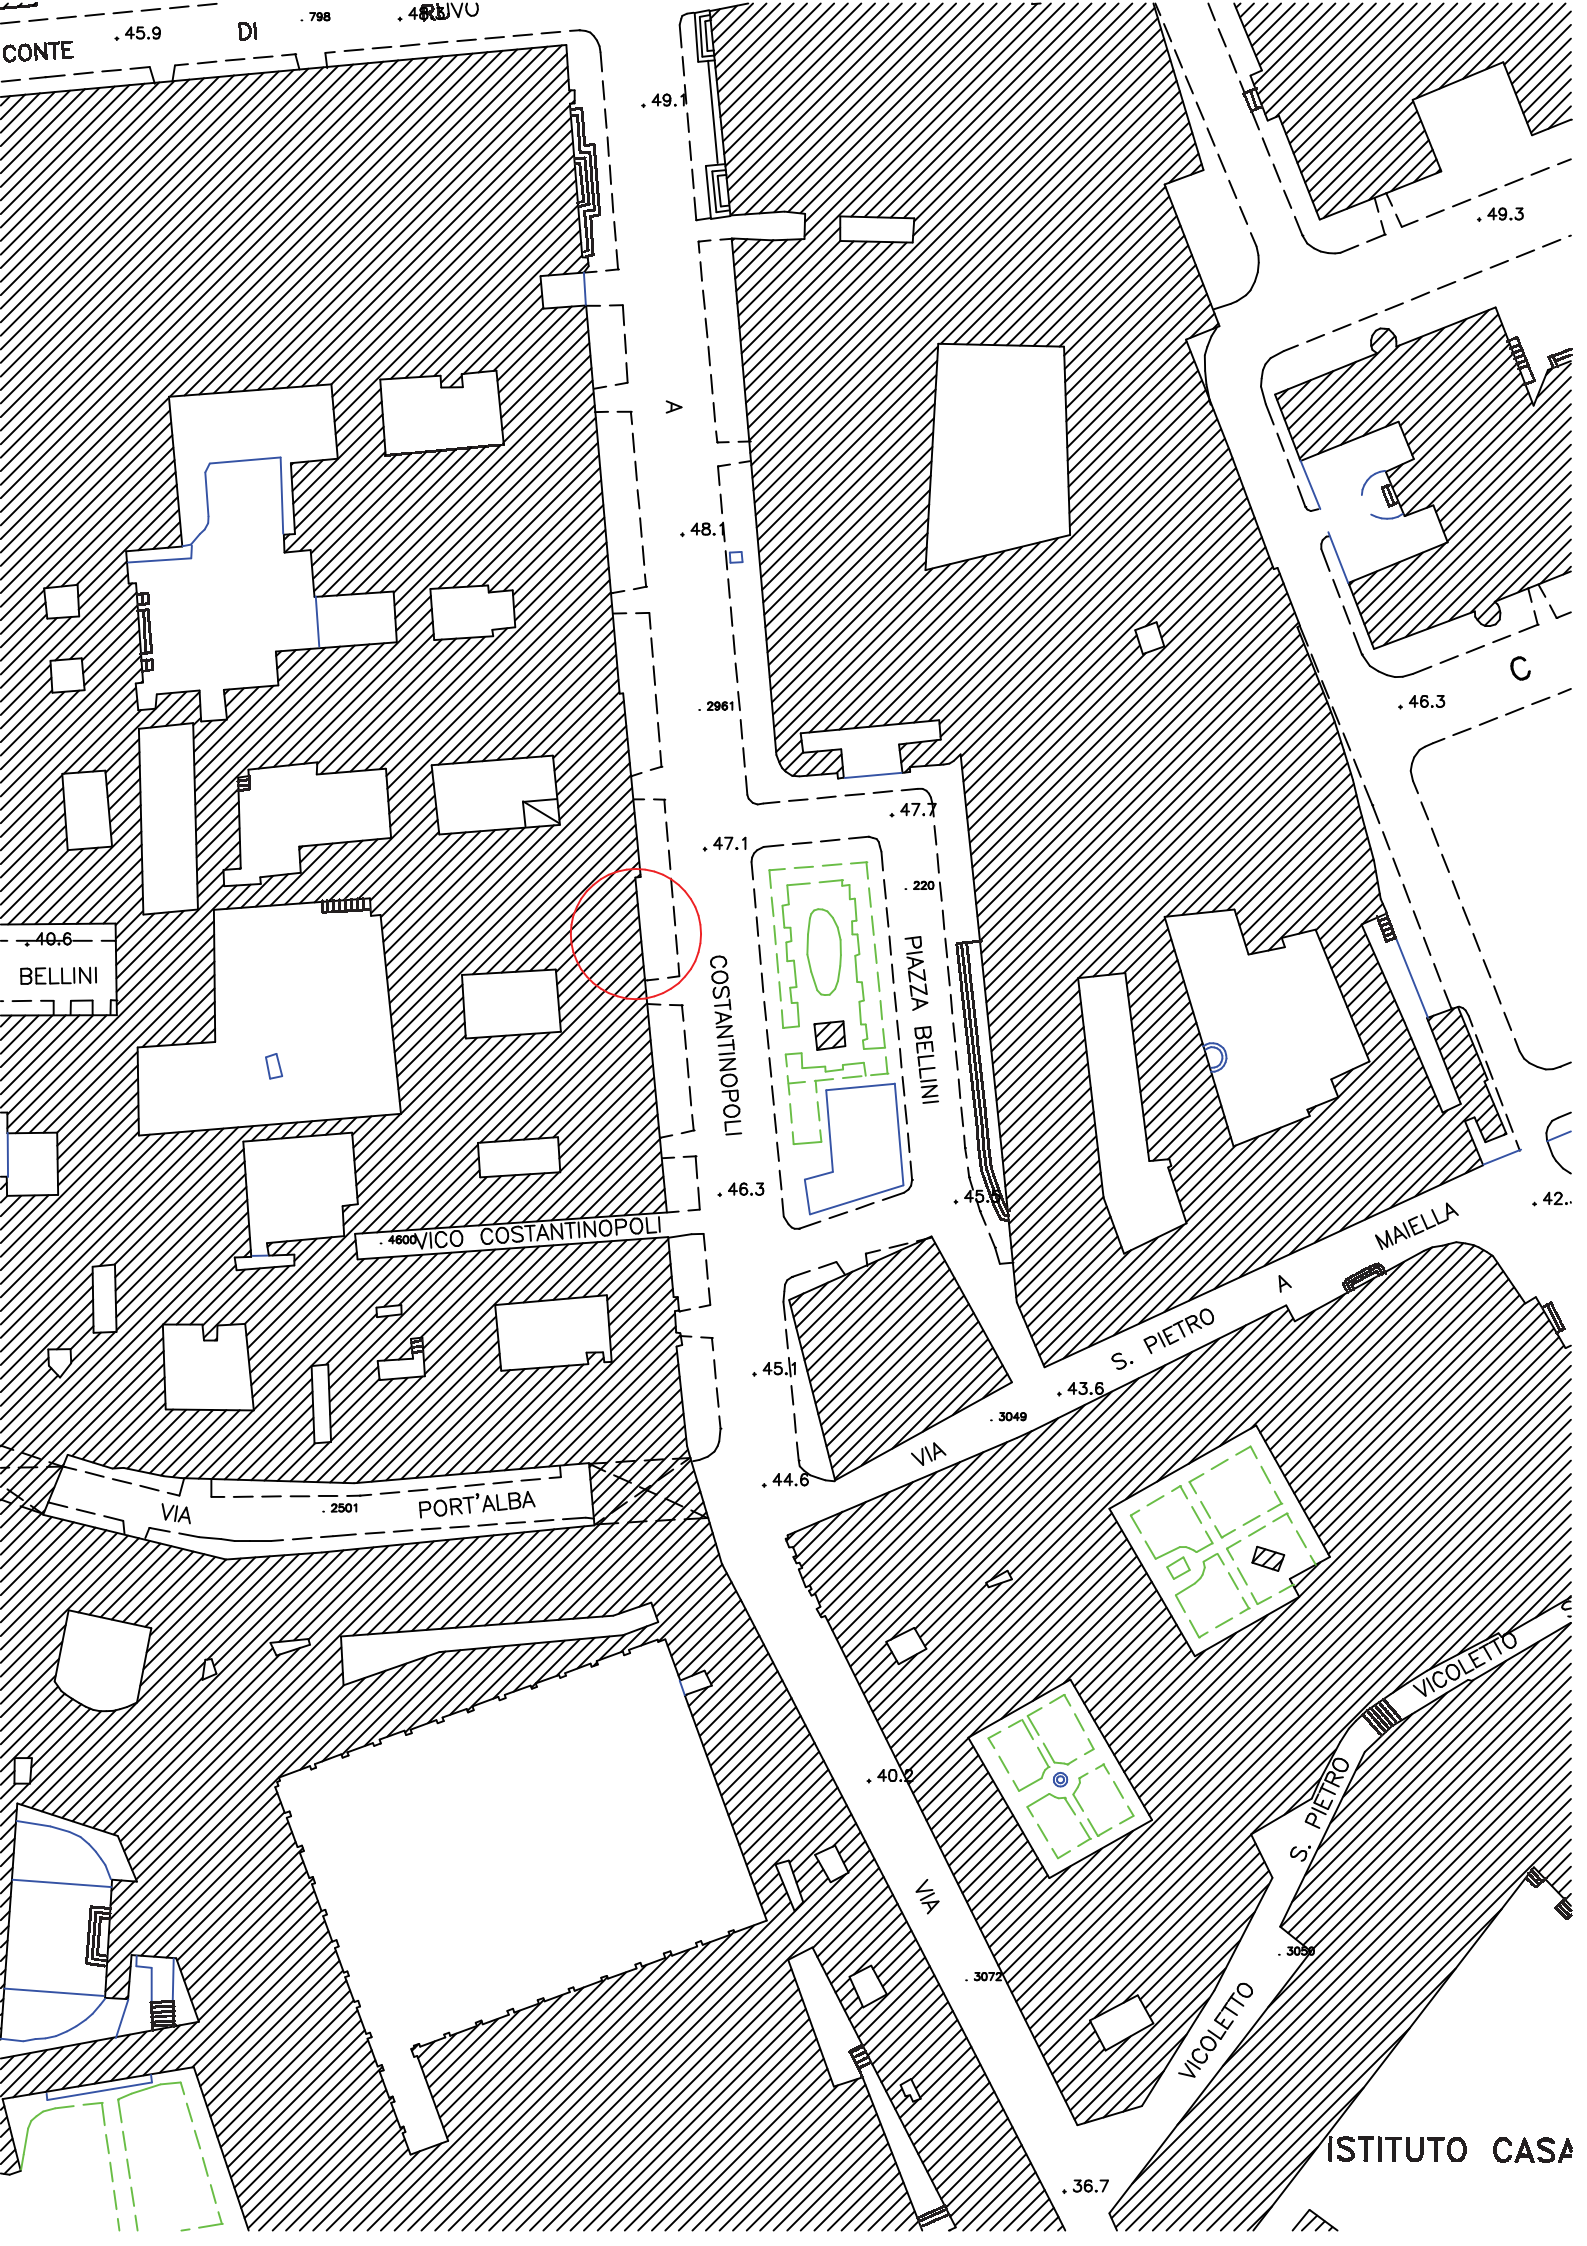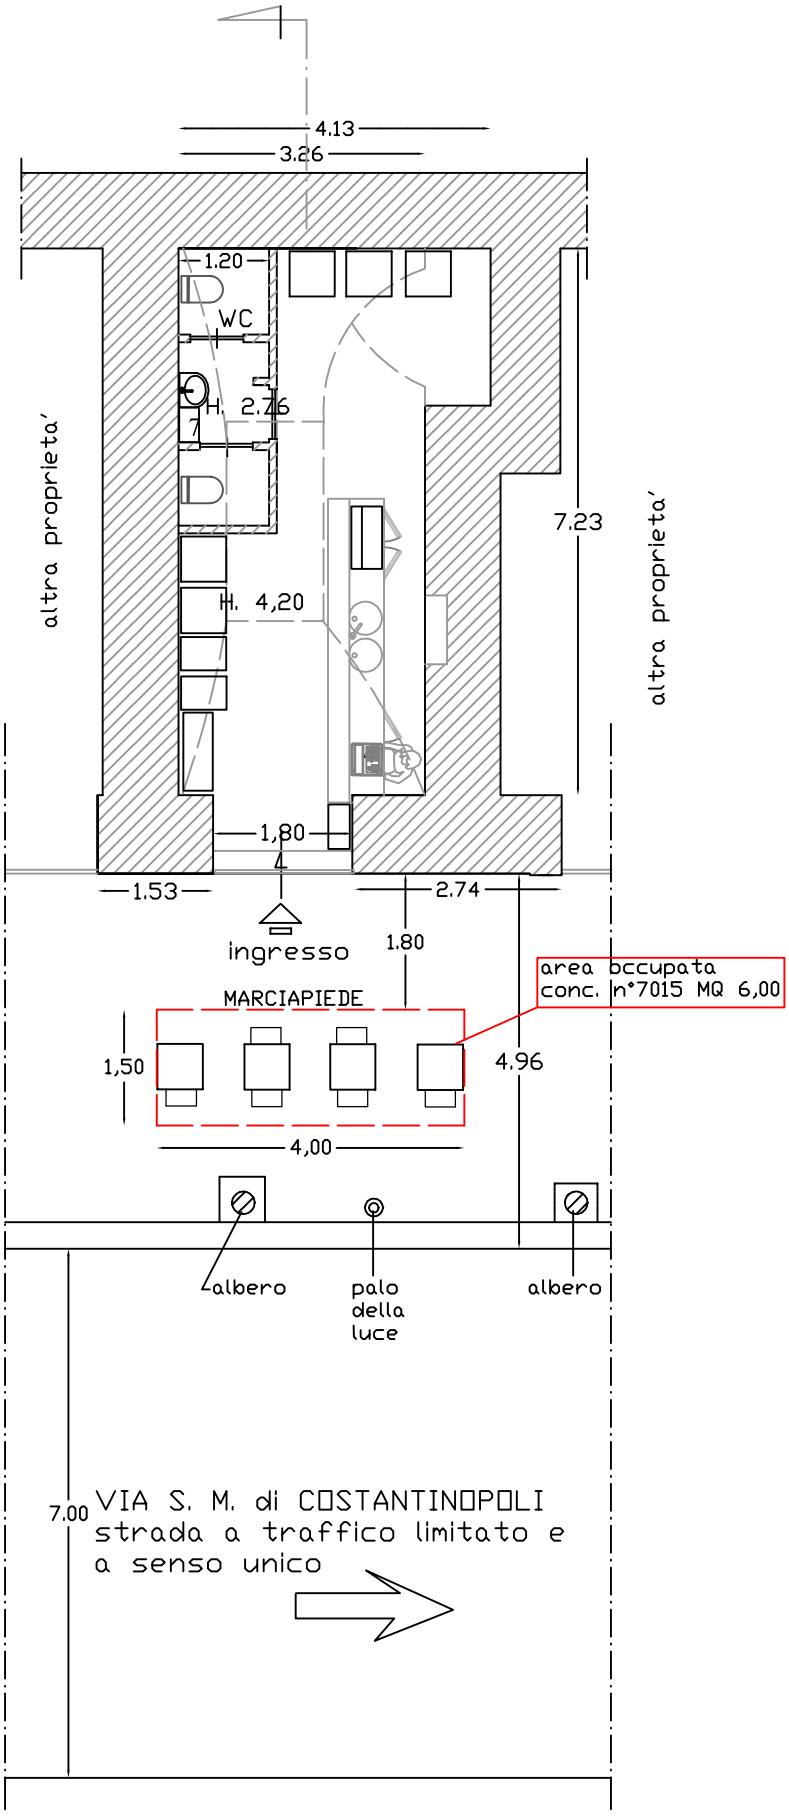


PLANIMETRIA DI RILIEVO CON OCCUPAZIONE
CONCESSA N° 7015 del 13-06-2020- SCALA 1:100

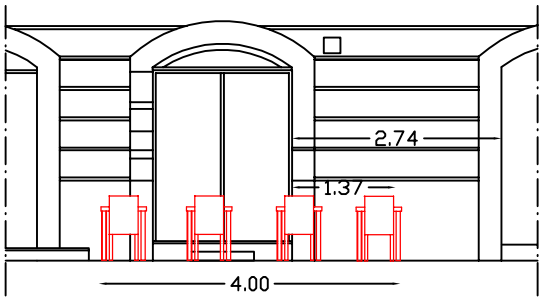

PROSPETTO DI RILIEVO- SCALA 1:100

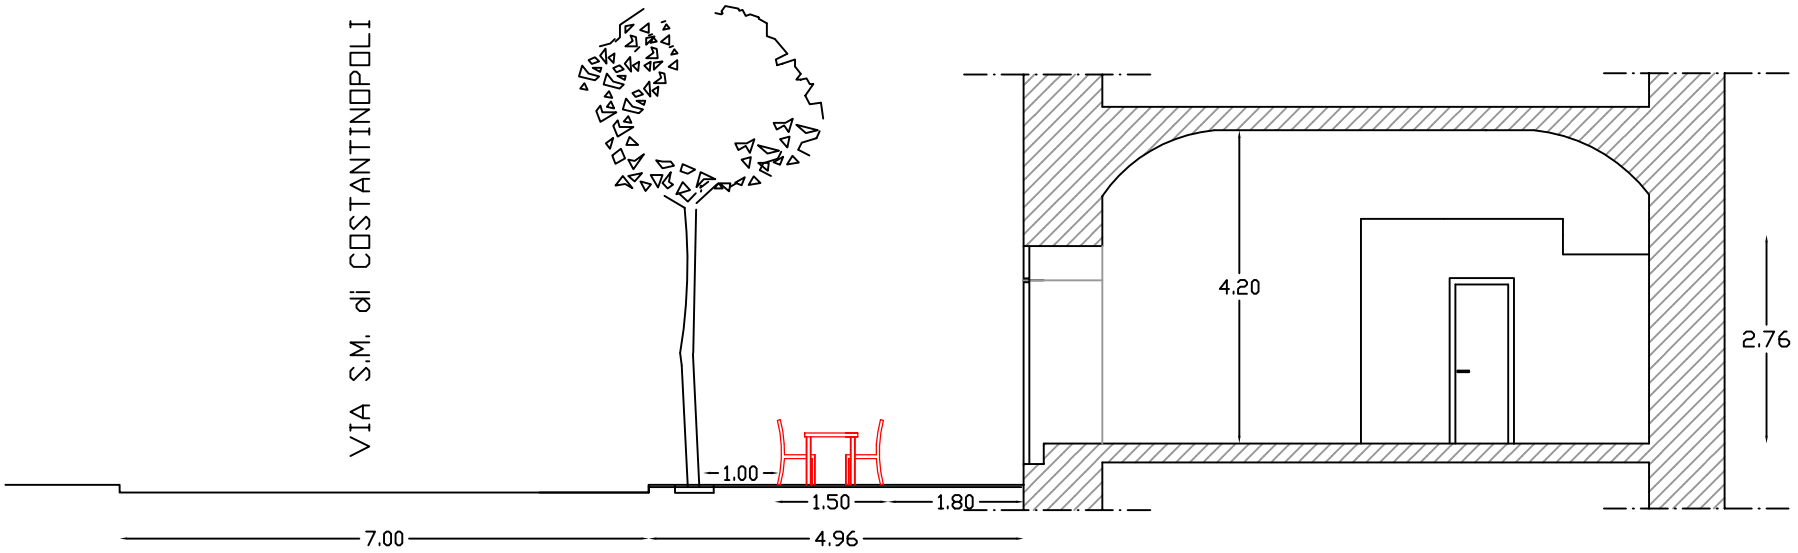


SEZIONE DI RILIEVO SCALA 1:100

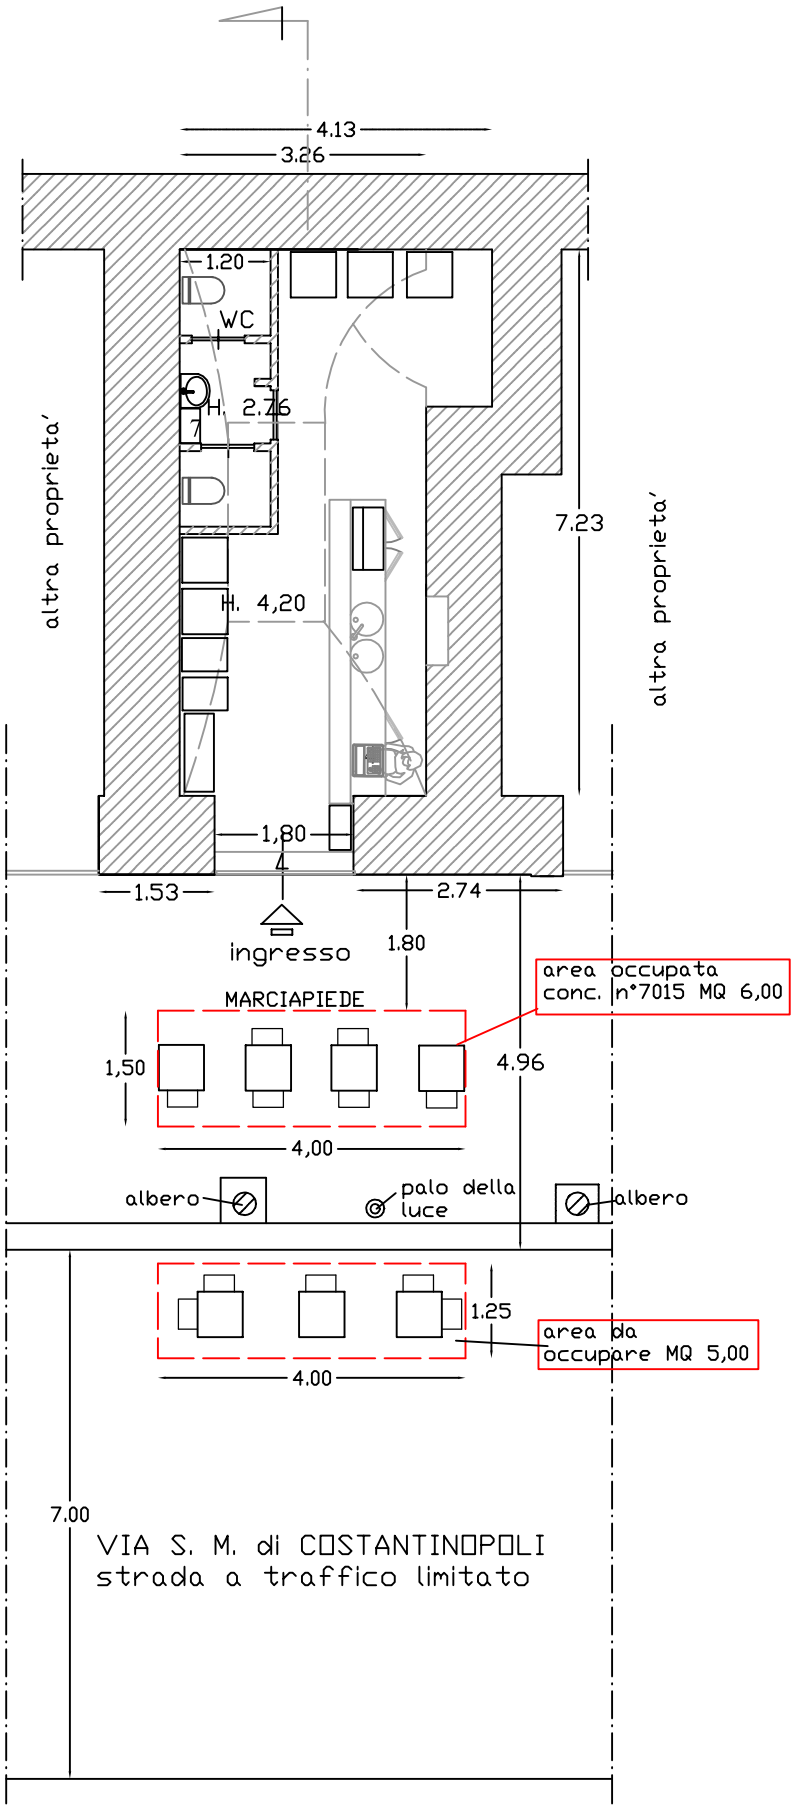

PLANIMETRIA DI PROGETTO DELL'AREA DA OCCUPARE
- SCALA 1:100



PROSPETTO DI PROGETTO DELL'AREA DA OCCUPARE
- SCALA 1:100

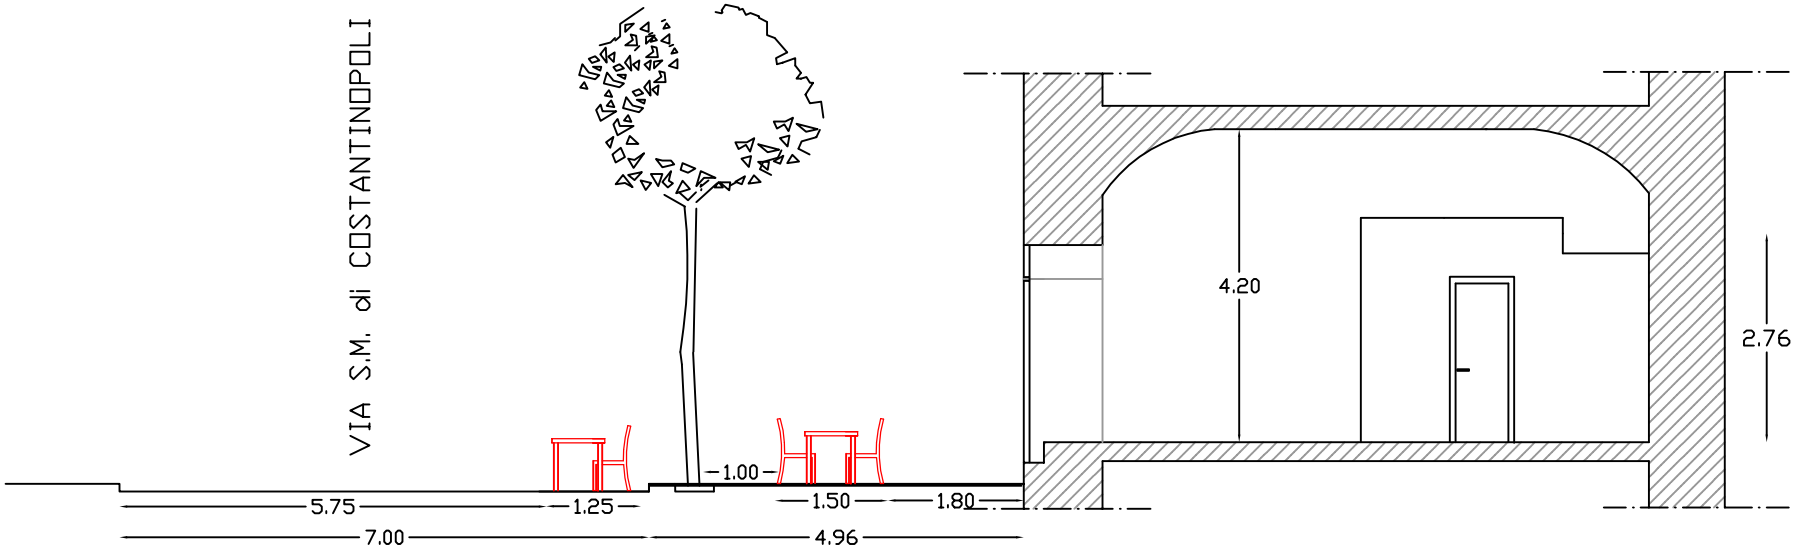

SEZIONE DI PROGETTO SCALA 1:100